La Mangeoire — Bar · plan coté

Vue de dessus, échelle 1/30 sur A4 · même orientation que le plan Kieffer (cuisine à gauche, entrée 2 en bas)

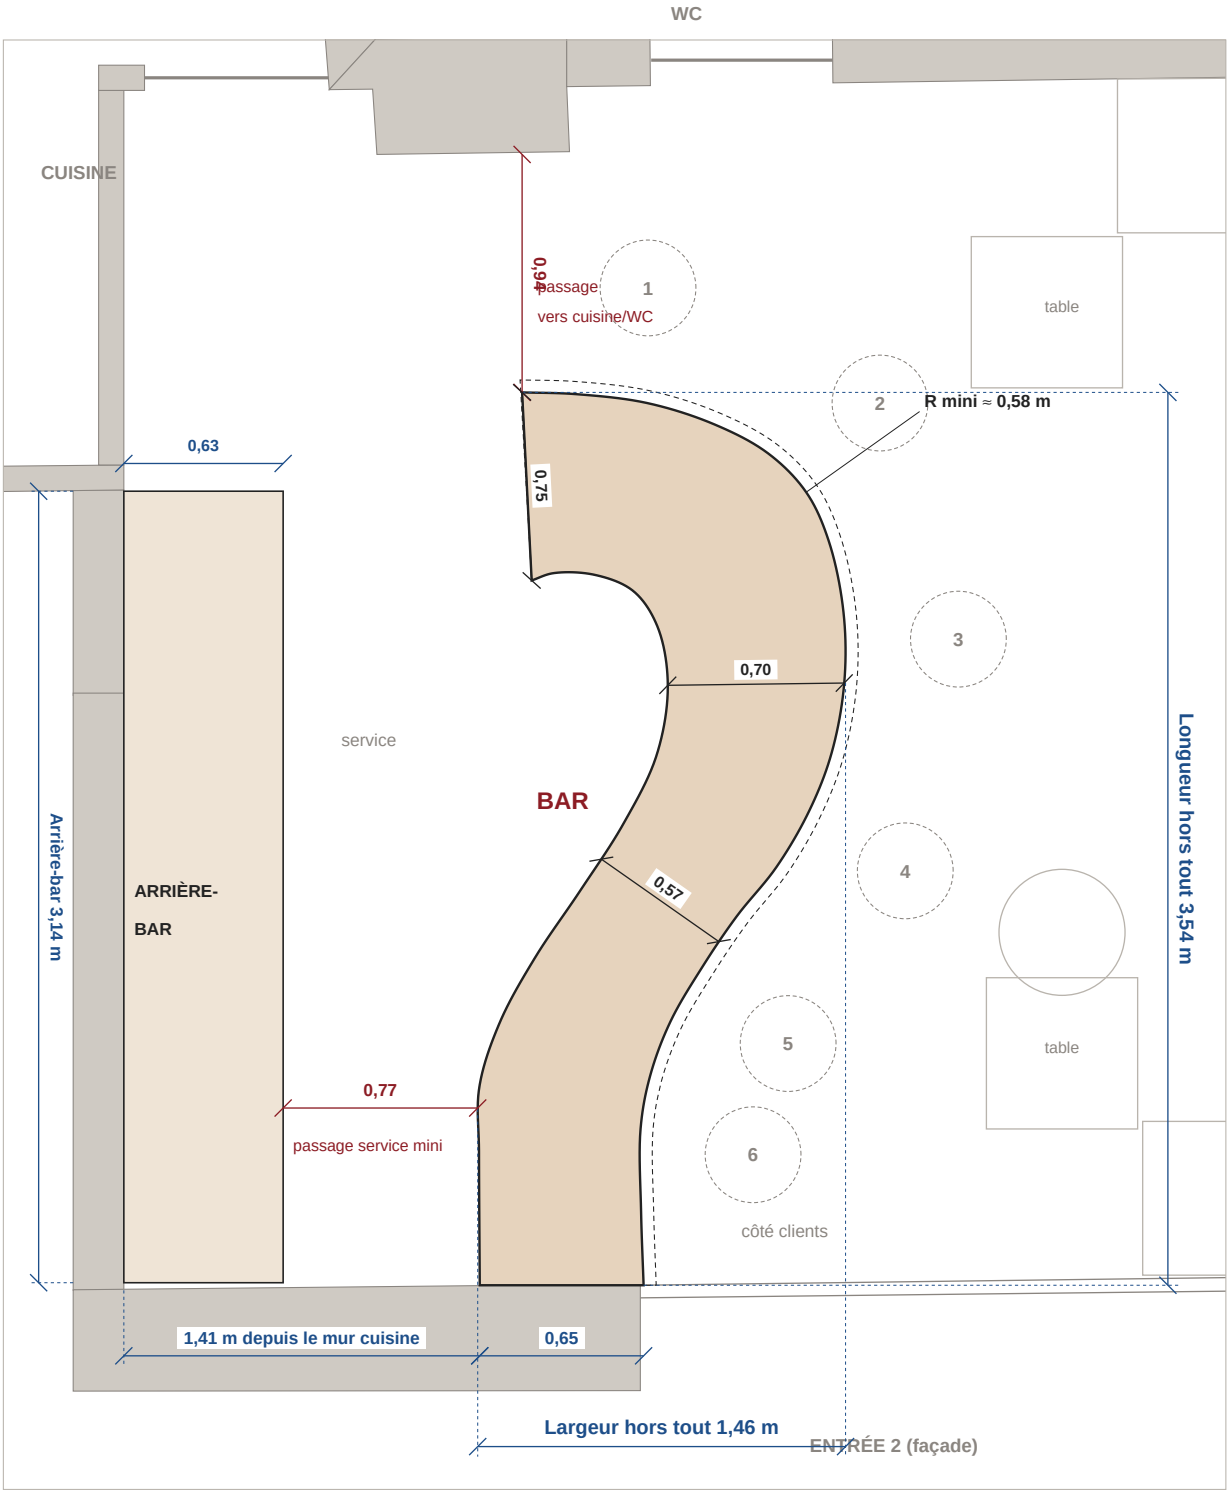

Échelle 1/30

0 — 2,5 m

À retenir

- Développé côté clients (face galbée) : 4,62 m · côté service : 3,40 m · profondeur du comptoir 0,57 à 0,78 m (env. 0,70 m).
- Le bar part du mur de façade (entrée 2) sur 0,65 m et se termine en crochet côté cuisine ; plateau débordant de 5 cm côté clients (pointillés).
- 6 tabourets (cercles numérotés, Ø 38 cm) espacés d'environ 0,95 m ; tabouret 6 très proche du 5 (0,46 m), à repositionner ou supprimer.
- Points serrés : tabouret 2 à ~18 cm de la table près des WC ; tabouret 4 à ~23 cm de la chaise de la table près de l'entrée 2.

La Mangeoire — Bar · coupe et arrière-bar

Coupe type du comptoir au 1/15 · élévation de l'arrière-bar au 1/30 · hauteurs en mètres

Coupe type A-A (au 1/15)

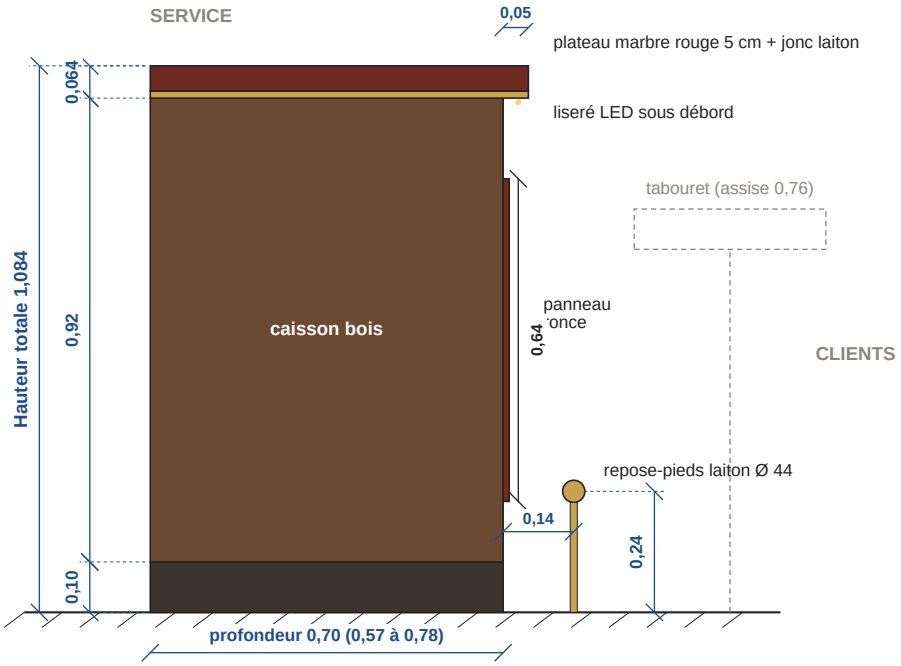
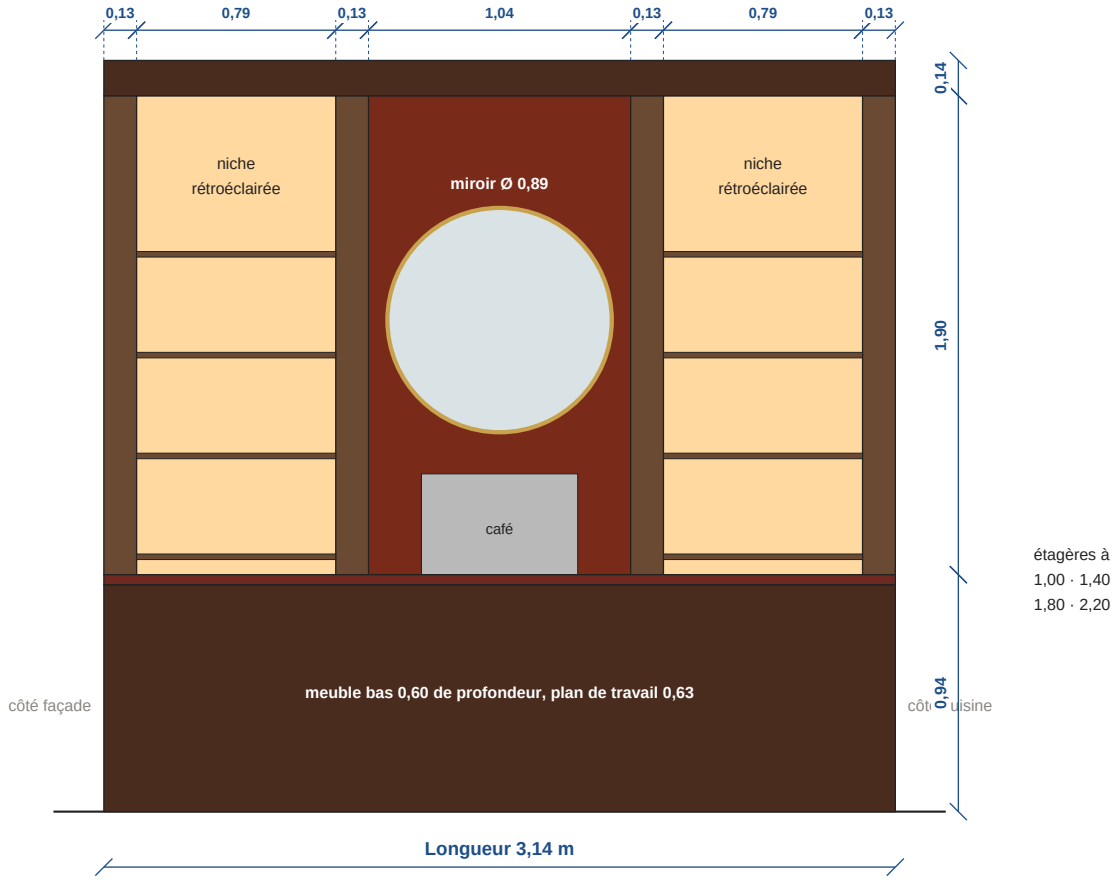
Arrière-bar · élévation vue du service (au 1/30)